




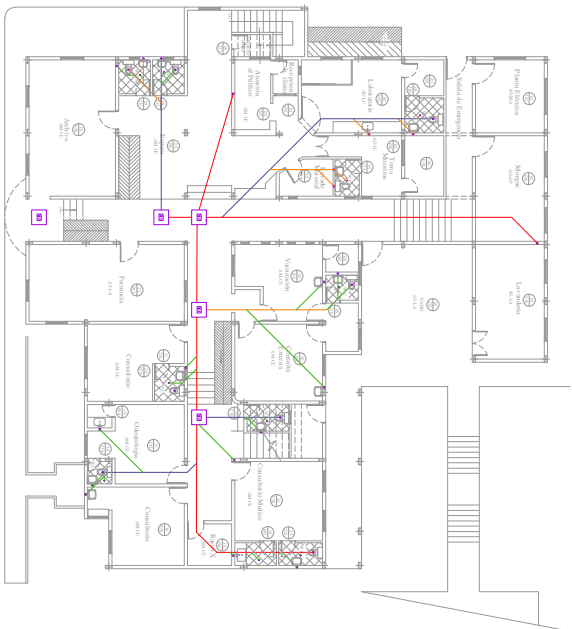

PLANTA DESA/DES PRIMER NIVEL
Escala 1:100

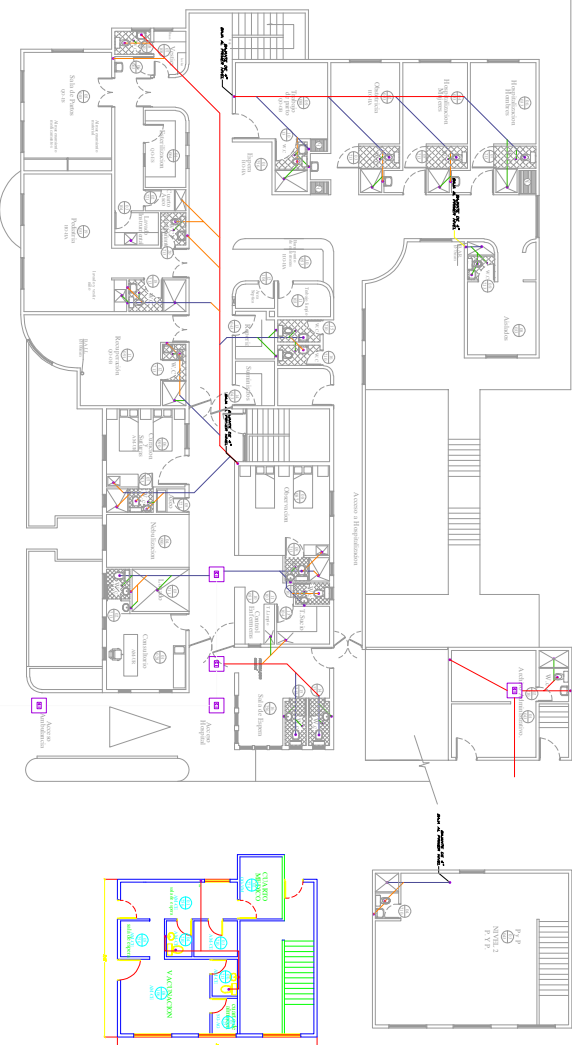

PLANTA DESA/DES TERCER NIVEL
Escala 1:100

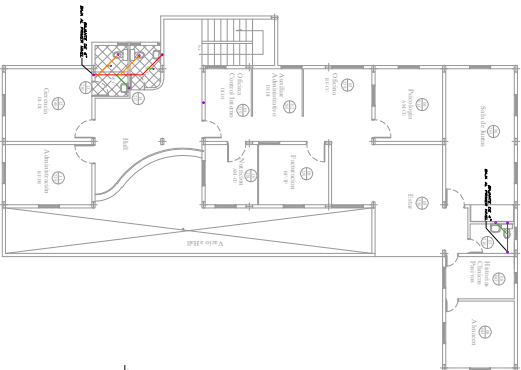

PLANTA DESA/DES SEGUNDO NIVEL
Escala 1:100

CONVENCIONES	
REGULA	•
CAJA DE INSPECCION	C1
DESAGUE AGUA SERVIDA	•
SANITARIA DE 6"	—
SANITARIA DE 4"	—
SANITARIA DE 3"	—
SANITARIA DE 2"	—
SANITARIA DE 1 1/2"	—

CUADRO CONVENCIONES

CATASTRO FISICO HOSPITALARIO	
DEPARTAMENTO	ANTIOQUIA
MUNICIPIO	BRICENO
INSTITUCION	FL. SAGRADO CORAZON
SEDE	UNICA
EDIFICIO	PSO 011
SECCION	011
PLANO	024
DE	027
RESPONSABLE	
FINA	
FECHA	MARZO/2012
TITULO DE MODIFICACION	LEVANTAMIENTO ACTUALIZADO
ELABORADO	HERNAN DABO SEPULVEDA Z